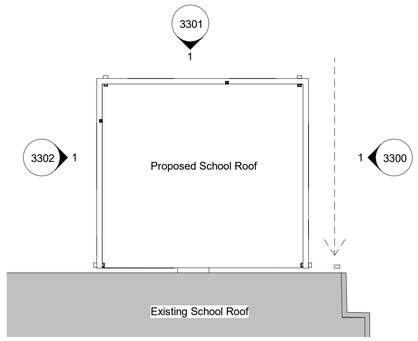

Elevation Location plan
1 : 200

DO NOT SCALE FROM THIS DRAWING EXCEPT FOR PLANNING PURPOSES ONLY
Copyright reserved

This drawing is issued for the sole & exclusive use of the named recipient. Distribution to any third party is on the strict understanding that no liability is accepted by YMD Boon Ltd for any discrepancies, errors or omissions that may be present & no guarantee is offered as to the accuracy of information shown.
All dimensions to be checked on site & any discrepancies found shall be brought to the attention of YMD Boon Ltd prior to commencement of any building works.

THIS DRAWING IS TO BE READ IN COLOUR PRINT

CDM - RESIDUAL RISKS
The following are considered to be significant risks relevant to this drawing, which could not be fully mitigated or removed through design. Further possible control measures have been identified within the Design Risk Assessments which may help to mitigate these and other identified risks further during the construction / maintenance process.

ELEVATION LEGEND:

- Movement joint, refer to S.E. drawings and specification for details.
- ED 01 — External Door Reference
- NW 01 — Window Reference

NOTES:

All levels / heights to be confirmed on site before work commences. Any discrepancies affecting the design must be reported to the Architect immediately.

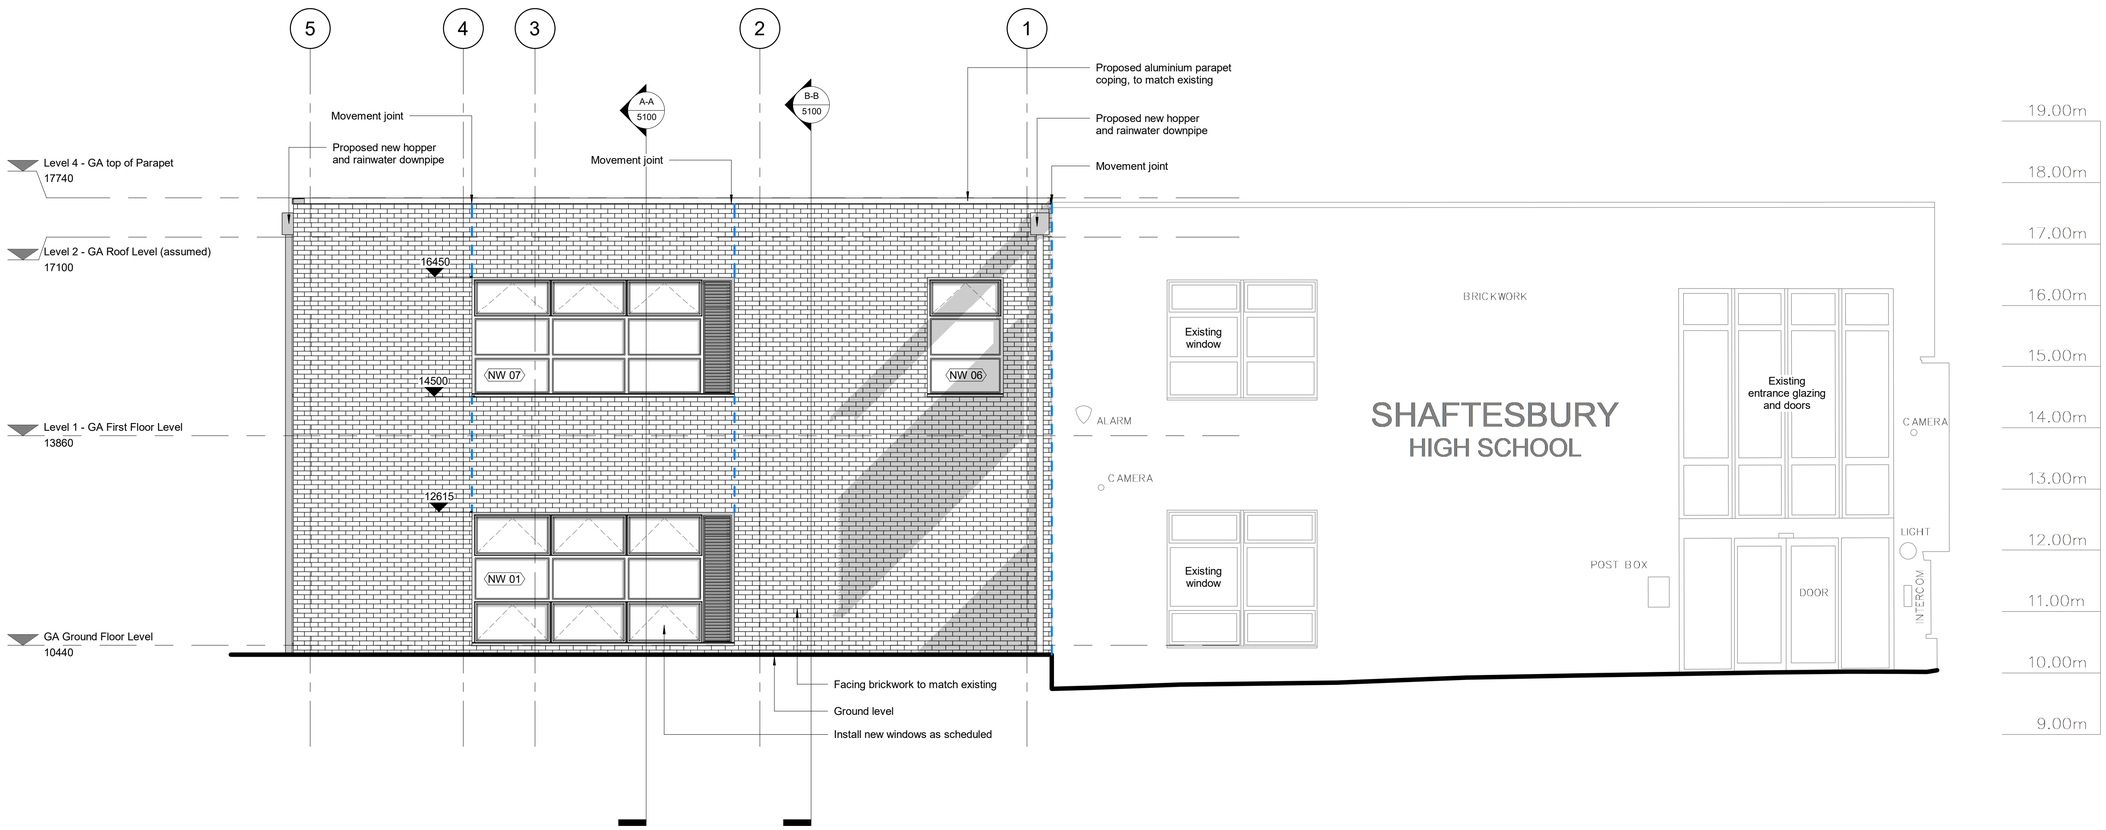

1 Proposed West Elevation
1 : 50

1m 5m

Rev		Date	Drawn	Chk'd
C01	Construction Issue	19.07.24	SK	KR

CONSTRUCTION

ymd boon Architects & Construction Consultants
6b Anson House, Compass Point Business Park
Market Harborough, LE16 9HW
Ground Floor, Loxley House, Tottle Road, Nottingham, NG2 1RT
Oak House Buisness Centre, Waterside South, Lincoln, LN5 7FB

Client
Harrow Council

Project
Shaftesbury High School

Scale	Date	Drawn
As indicated @A1	**October 2023**	**SPD**
Drawing Title: **Proposed West Elevation**		Checked: **SK**
Drawing Number: **J4715-YMD-01-XX-DR-A-3302**	Status: **S3**	Revision: **C01**