DO NOT SCALE FROM THIS DRAWING EXCEPT FOR PLANNING PURPOSES ONLY
Copyright reserved

This drawing is issued for the sole & exclusive use of the named recipient. Distribution to any third party is on the strict understanding that no liability is accepted by YMD Boon Ltd for any discrepancies, errors or omissions that may be present & no guarantee is offered as to the accuracy of information shown.
All dimensions to be checked on site & any discrepancies found shall be brought to the attention of YMD Boon Ltd prior to commencement of any building works.

THIS DRAWING IS TO BE READ IN COLOUR PRINT

CDM - RESIDUAL RISKS
The following are considered to be significant risks relevant to this drawing, which could not be fully mitigated or removed through design. Further possible control measures have been identified within the Design Risk Assessments which may help to mitigate these and other identified risks further during the construction / maintenance process.

Door Type Elevation Views

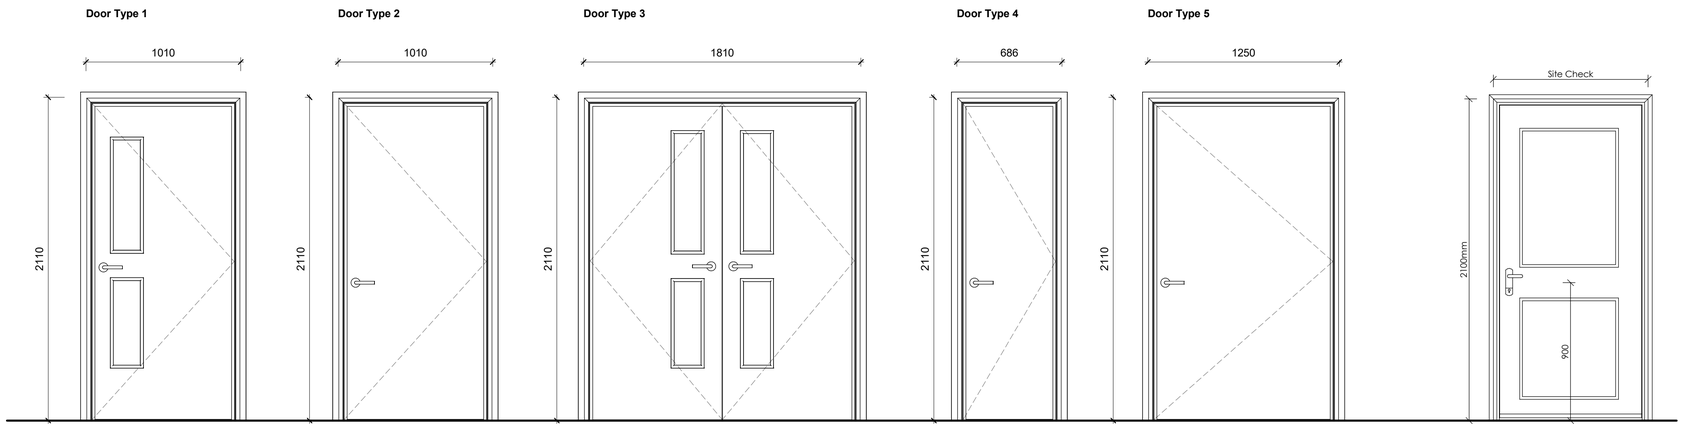

DOOR TYPE 6
External Door with
FE Ironmongery

NOTE: New aluminium door to existing opening.
Site check required.

Door Ref: ED01
External single door (glazed panels) – Smart Door or similar.
Smart Innovation Centre,
Church Street,
Darfield,
Barnsley S73 9LG
T: 01226 731333
helpdesk@smartdoorsolutions.co.uk

Note: Door to open outwards, RH Swing.
To include weather cill & seals & Push pad opening, complete with Exidor external opening device from Assa Abloy or similar.

Door Type - Plan Views

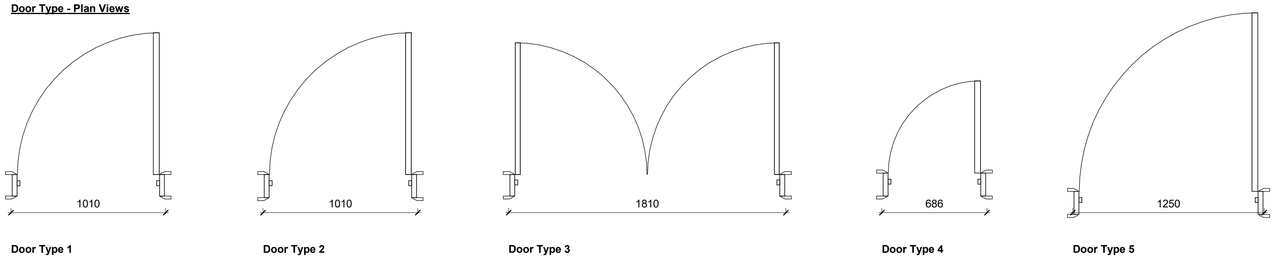

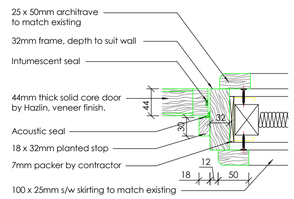

Internal Door Jamb Detail
1 : 5

Door Schedule

Mark	YMD Door Type	To Room: Name	Width	Height	YMD Door Swing	YMD Door Finish	YMD Door Fire Rating	YMD Door Frame	YMD Door Glazing	YMD Door Ironmongery	Comments
ED 01	YMD Door Type 6	Stairwell	1000	2100	RHS	PPC Aluminium External Door - Colour to match Existing	N/A	PPC Aluminium	28mm thick - Laminated inner pane, Toughened outer pane	Refer to manufacturers details	
ND 01	YMD Door Type 5	Circulation	1250	2110	RHS	Formica Laminate Finish Colour TBC	FD30S	32 x 126mm sw	N/A	Set HD	Clear effective width of door to be 1000mm min
ND 02	YMD Door Type 1	Classroom 1	1010	2110	RHS	Formica Laminate Finish Colour TBC	FD30S	32 x 126mm sw	7mm AGC Glass UK - Pyrobelite 7	Set C3/C6	
ND 03	YMD Door Type 1	Classroom 2	1010	2110	LHS	Formica Laminate Finish Colour TBC	FD30S	32 x 126mm sw	7mm AGC Glass UK - Pyrobelite 7	Set C3/C6	
ND 04	YMD Door Type 1	Circulation	1010	2110	RHS	Formica Laminate Finish Colour TBC	FD30S	32 x 126mm sw	7mm AGC Glass UK - Pyrobelite 7	Set C3	
ND 05	YMD Door Type 3	Circulation	1810	2110	Double Door	Formica Laminate Finish Colour TBC	FD30S	32 x 126mm sw	7mm AGC Glass UK - Pyrobelite 7	Set P3	
ND 07	YMD Door Type 1	Sensory Room	1010	2110	LHS	Formica Laminate Finish Colour TBC	FD30S	32 x 126mm sw	7mm AGC Glass UK - Pyrobelite 7	Set C3	
ND 08	YMD Door Type 1	Classroom 3	1010	2110	RHS	Formica Laminate Finish Colour TBC	FD30S	32 x 126mm sw	7mm AGC Glass UK - Pyrobelite 7	Set C3/C6	
ND 09	YMD Door Type 1	Classroom 4	1010	2110	LHS	Formica Laminate Finish Colour TBC	FD30S	32 x 126mm sw	7mm AGC Glass UK - Pyrobelite 7	Set C3/C6	
ND 10	YMD Door Type 1	Meeting / Office	1010	2110	RHS	Formica Laminate Finish Colour TBC	FD30S	32 x 126mm sw	7mm AGC Glass UK - Pyrobelite 7	Set A3	
ND 11	YMD Door Type 3	Circulation	1810	2110	Double Door	Formica Laminate Finish Colour TBC	FD30S	32 x 126mm sw	7mm AGC Glass UK - Pyrobelite 7	Set P3	
ND 12	YMD Door Type 2	Disabled WC	1010	2110	RHS	Formica Laminate Finish Colour TBC	FD30S	32 x 126mm sw	N/A	Set HD	Doc M pack
ND 13	YMD Door Type 2	Circulation	1010	2110	LHS	Formica Laminate Finish Colour TBC	FD60S	32 x 126mm sw	N/A	Set M3	
ND 14	YMD Door Type 4	Store	686	2110	LHS	Formica Laminate Finish Colour TBC	FD30S	32 x 126mm sw	N/A	Set A3	

FOR IRONMONGERY SETS PLEASE REFER TO ASPEX DOCUMENT - YMD BOON - EDUCATION SETS DOCUMENT_REV A

1m 10m

Rev		Date	Drawn	Chk'd
C01	Construction Issue	19.07.24	SK	KR

CONSTRUCTION

ymd boon Architects & Construction Consultants
6b Anson House, Compass Point Business Park
Market Harborough, LE16 9HW
Ground Floor, Loxley House, Tottle Road, Nottingham, NG2 1RT
Oak House Buisness Centre, Waterside South, Lincoln, LN5 7FB

Client
Harrow Council

Project
Shaftesbury High School

Scale	Date	Drawn
As indicated @A1	**June '23**	**SPD**
Drawing Title: **Door Schedule**		Checked: **SS**

Drawing Number	Status	Revision
J4715-YMD-01-XX-DR-A-8200	**S3**	**C01**