


The windows and doors to the south and west elevation will be white aluminium framed.  
There are no new windows to the east elevation.  
The windows to the south elevation will follow the profile of the proposed new building giving the building transparency giving both elevations and building a contemporary feel.

Levels 0 - 6 are based on the finished floor levels of the existing building. The FFL (Level 1) is approximately 100mm above ground level at the entrance door. Spot levels for the height above sea level are shown on the plan drawings.

The ridge to the new entrance building is the same as the existing chapel 5183mm above the FFL. The finished ridge level is below the 25 degree rule angle measured from the centre line of the adjacent property.

Please Note:  
Front and Rear extensions / porches to houses have not been shown  
Railing and gates to Church property have not been shown

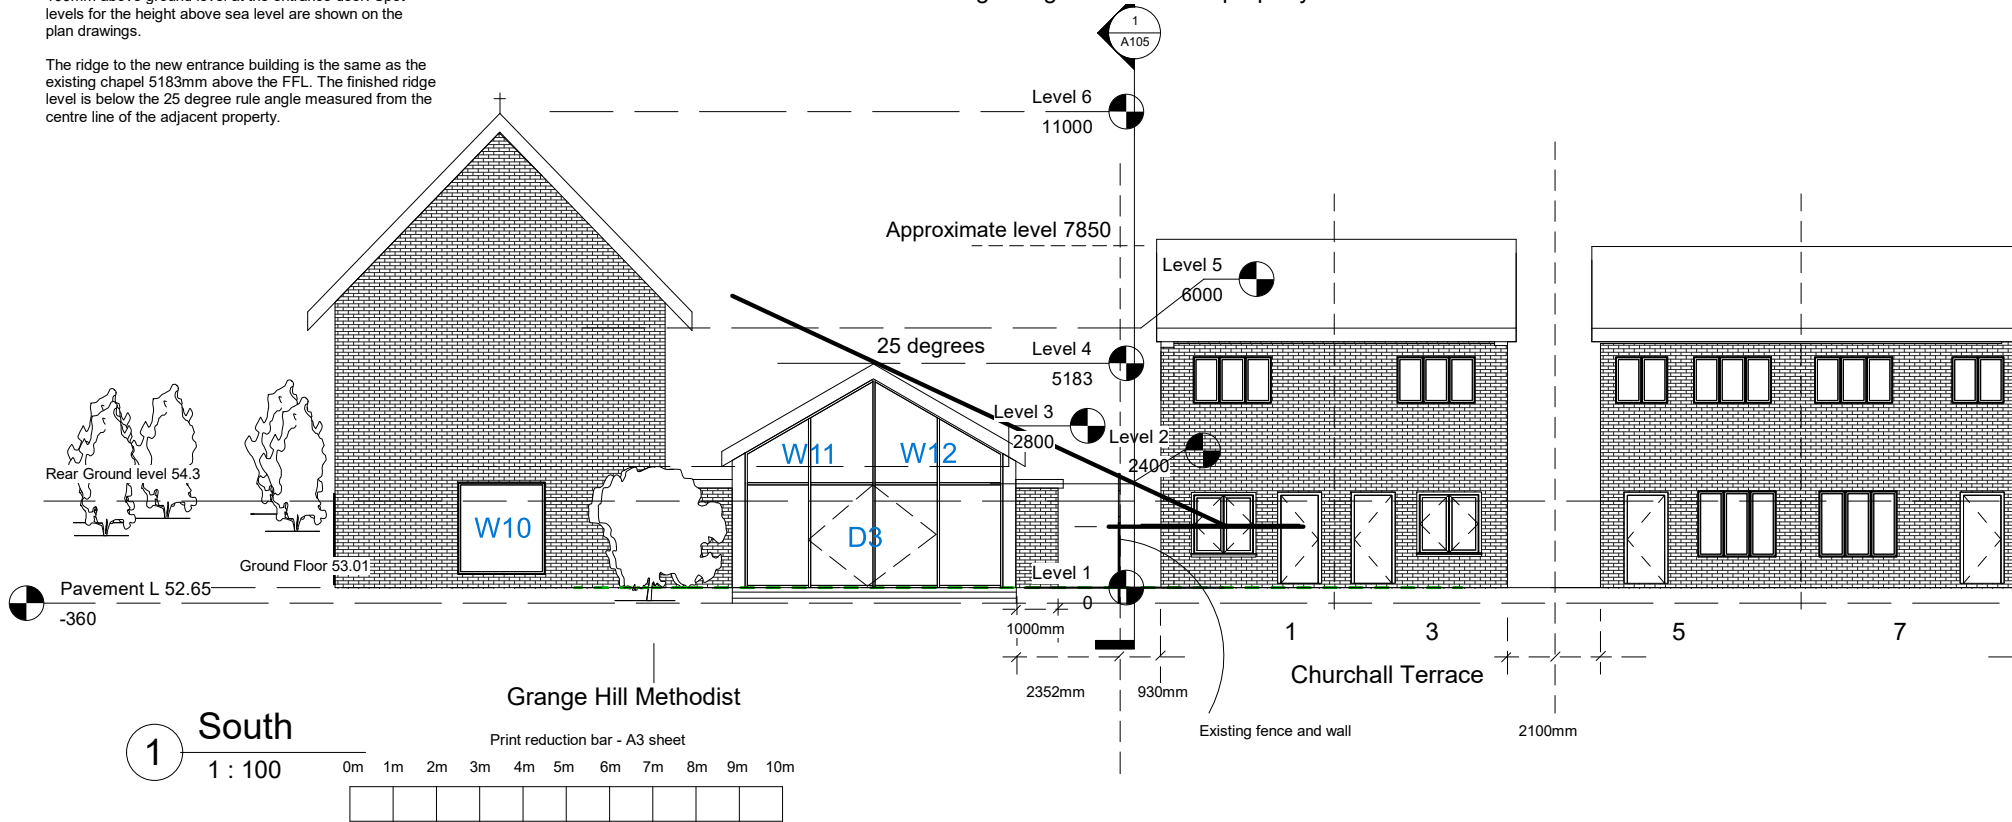

|   |  |      |           |      |   |                               |
|---|--|------|-----------|------|---|-------------------------------|
| CLIENT: Grange Hill Methodist Church                                                                           |  | Rev. | AMENDMENT | DATE | Grange Hill Methodist church<br>Burrow Road, Chigwell, Essex IG7 4HQ<br>Proposed Front - (South Elevation) (Showing all adjacent houses) |                               |
| File: New entrance 2025 - 26 with 1 Churchall Terrace - A101<br>Barking, Dagenham and Ilford Methodist Circuit |  |      |           |      | SCALE: 1 : 100   | 16 June 2026 - Rev 8          |
|   |  |      |           |      | DRAWN M. Dawson   | JOB / DRAWING No. GH 007 (R8) |
|   |  |      |           |      |   | REVISION 8                    |
|   |  |      |           |      |   |                               |
|   |  |      |           |      |   |                               |
| ALL RIGHTS RESERVED THE COMPANY. NO REPRODUCTION UNLESS WRITTEN CONSENT GIVEN                                  |  |      |           |      |   |                               |