


EXTERNAL WINDOWS

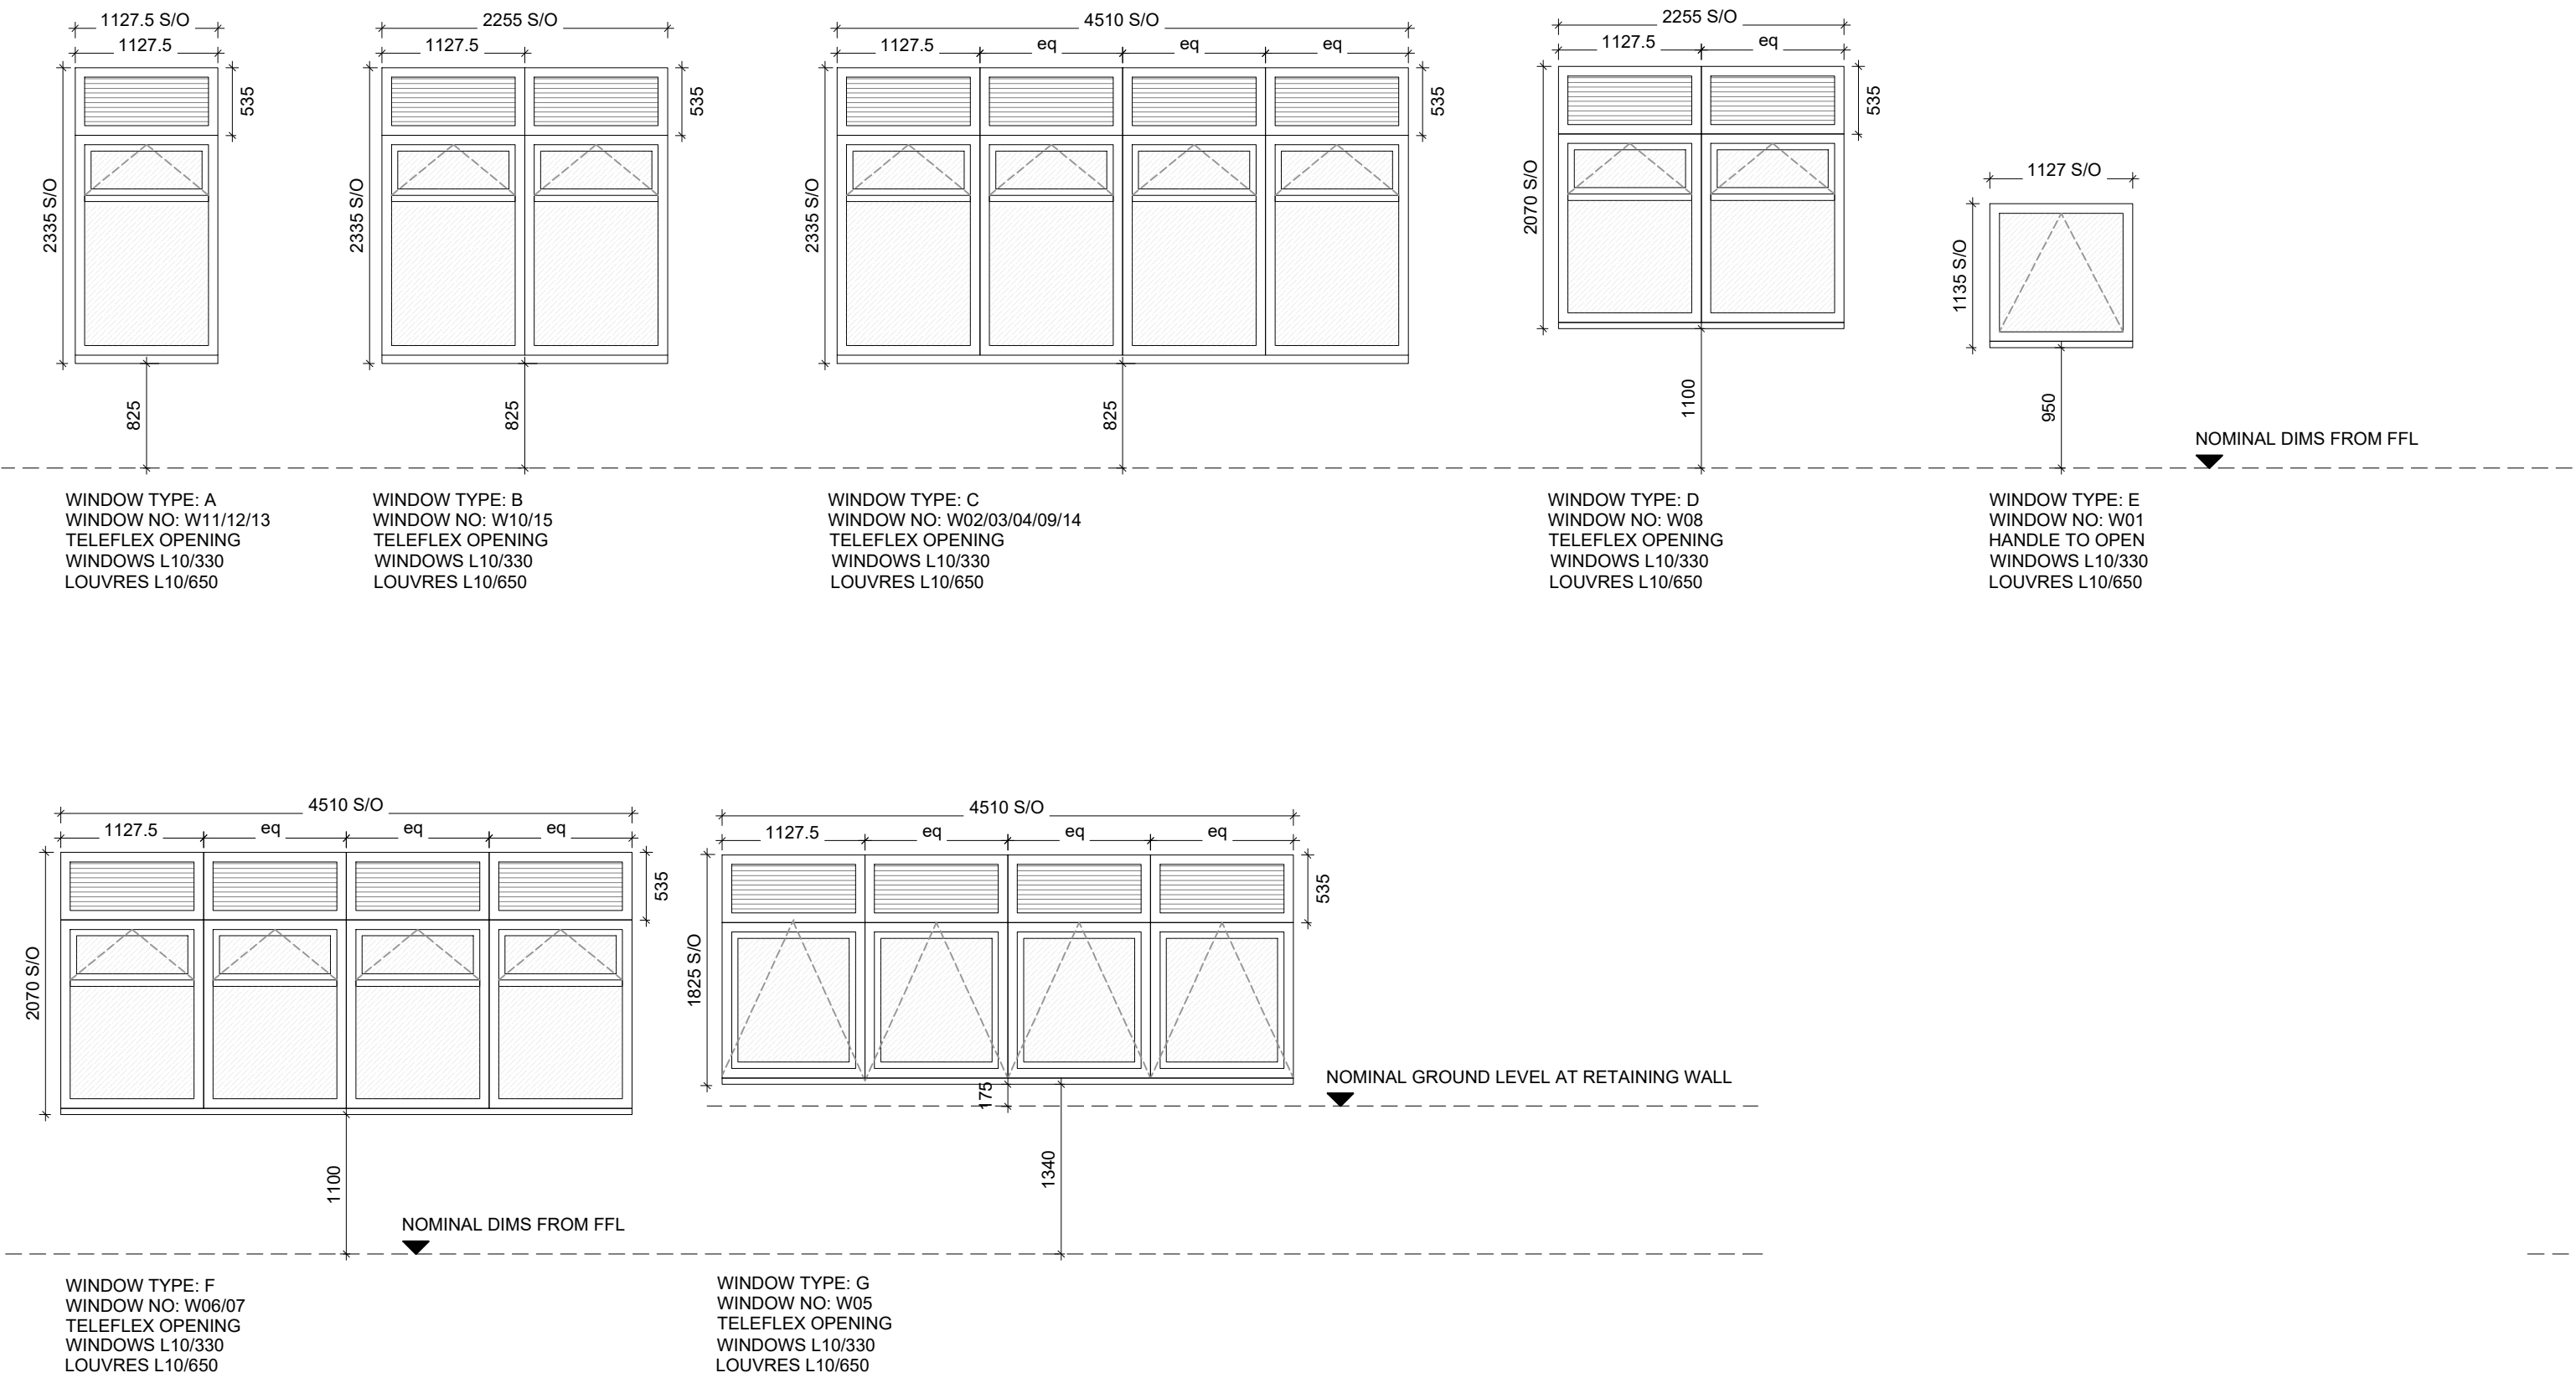

DRAWING NOTES 1. filename: 1118 Window Schedule CW.dwg 2. Do not scale this drawing in either paper or digital form. Use figured dimensions only. Detailed site survey to be carried out to establish tolerances. Figured dimensions are in mm. All dimensions shall be verified on site before proceeding with the work. The architect shall be notified of any discrepancies. 3. This drawing has been produced for sole use on this project and is not intended for use by any other person or for any other purpose. © Copyright RSS (U.K.) 4. All printed copies should be made at 100% of the original page size. Use scale bars, where included, to check that the drawing has been printed to the intended scale as identified in the drawing title block. 5. This drawing is not intended for construction unless specifically described as such.		REVISIONS <table><tr><th>REV</th><th>DATE</th><th>STATUS</th></tr><tr><td>T01</td><td>03.10.25</td><td>Issued for Tender</td></tr></table> Changes since last issue: -		REV	DATE	STATUS	T01	03.10.25	Issued for Tender	Notes: - This drawing is issued for Tender purposes - Please read alongside Window Schedule for specification		28 NAVIGATION ROAD LONDON E3 3TG T : 020 7739 8945 E : rss@rssa.co.uk www.rivingtonstreetstudio.co.uk rivingtonstreetstudio									
REV	DATE	STATUS																			
T01	03.10.25	Issued for Tender																			
				job title		Stoke Park School Expansion															
				drawing title		Window Types 1															
drawn by		job no.		suitability		revision		PROJECT		ORIGIN.		VOLUME		LEVEL		TYPE		ROLE		NUMBER	
CW		1118		D2		T01		SPS		_ RSS		_ XX		_ ZZ		_ DR		_ A		_ 4101	
scale		1:50																			

