


EXTERNAL WINDOWS

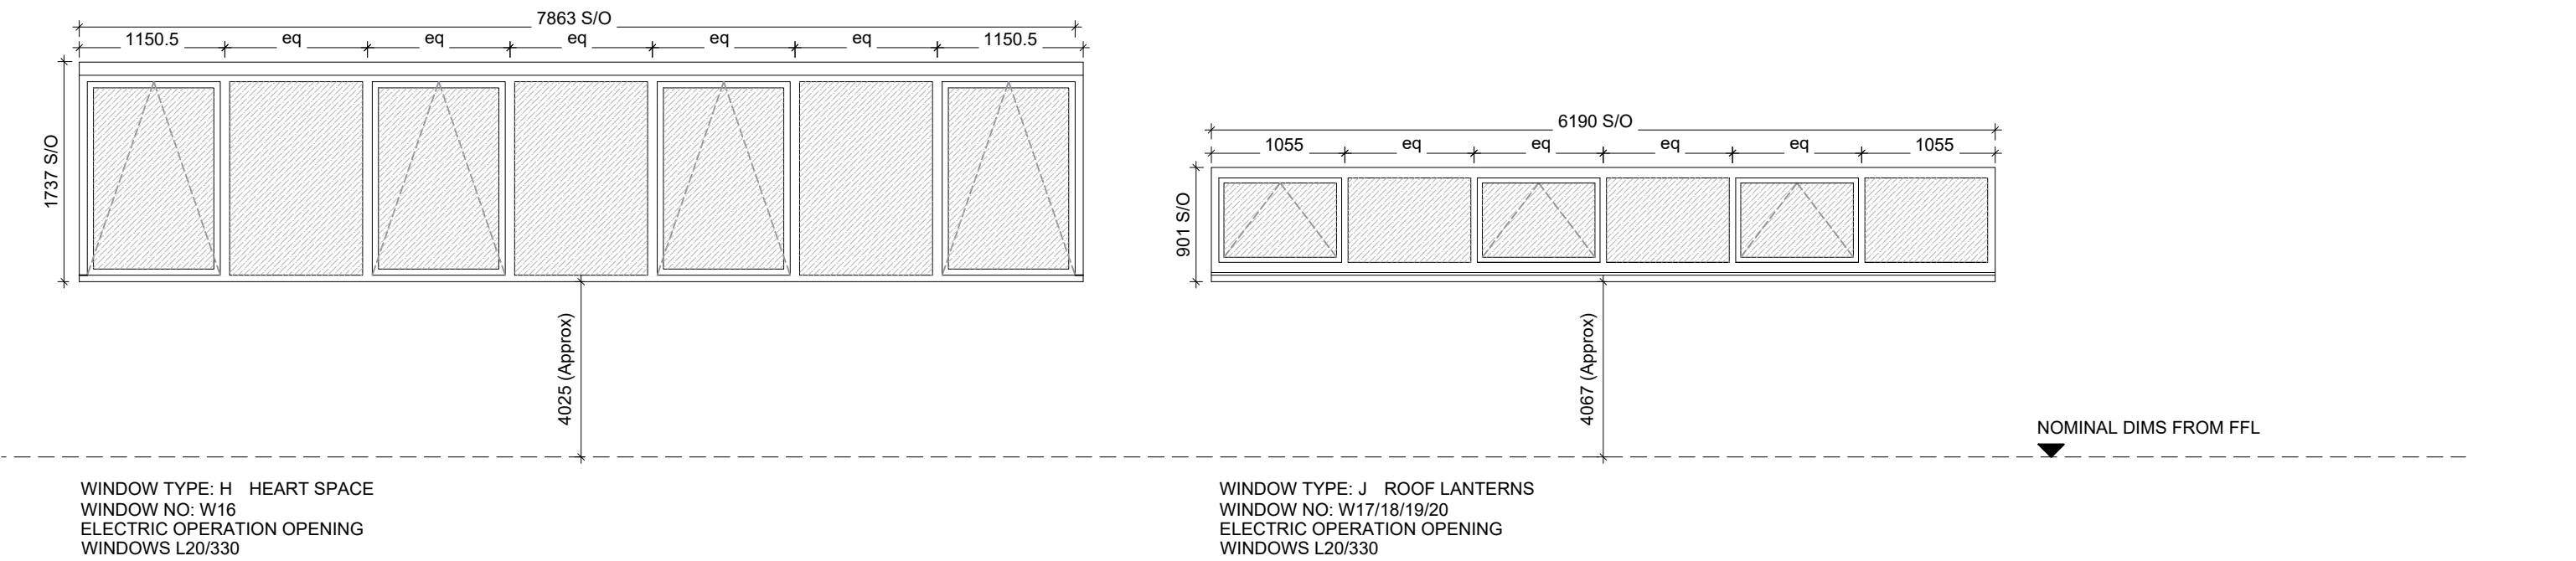

1150.5

eq

eq

eq

eq

eq

1150.5

7863 S/O

1737 S/O

4025 (Approx)

WINDOW TYPE: H HEART SPACE
WINDOW NO: W16
ELECTRIC OPERATION OPENING
WINDOWS L20/330

1055

eq

eq

eq

eq

1055

6190 S/O

901 S/O

4067 (Approx)

WINDOW TYPE: J ROOF LANTERNS
WINDOW NO: W17/18/19/20
ELECTRIC OPERATION OPENING
WINDOWS L20/330

NOMINAL DIMS FROM FFL

DRAWING NOTES

1. filename: 1118 Window Schedule.dwg

2. Do not scale this drawing in either paper or digital form. Use figured dimensions only. Detailed site survey to be carried out to establish tolerances. Figured dimensions are in mm. All dimensions shall be verified on site before proceeding with the work. The architect shall be notified of any discrepancies.

3. This drawing has been produced for sole use on this project and is not intended for use by any other person or for any other purpose. © Copyright RSS (U.K.)

4. All printed copies should be made at 100% of the original page size. Use scale bars, where included, to check that the drawing has been printed to the intended scale as identified in the drawing title block.

5. This drawing is not intended for construction unless specifically described as such.

REVISIONS

REV	DATE	STATUS
T01	03.10.25	Issued for Tender

Changes since last issue:
-

Notes:

- This drawing is issued for Tender purposes
- Please read alongside Window Schedule for specification

0

1m

2m

5m

28 NAVIGATION ROAD LONDON E3 3TG

T : 020 7739 8945

E : rss@rssa.co.uk

www.rivingtonstreetstudio.co.uk

rivingtonstreetstudio

job title

Stoke Park School Expansion

drawing title

Window Types 2

drawn by	job no.	suitability	revision	PROJECT	ORIGIN.	VOLUME	LEVEL	TYPE	ROLE	NUMBER
CW	1118	D2	T01	WRC	RSS	XX	ZZ	DR	A	4102

scale 1:50