


EXTERNAL DOORS

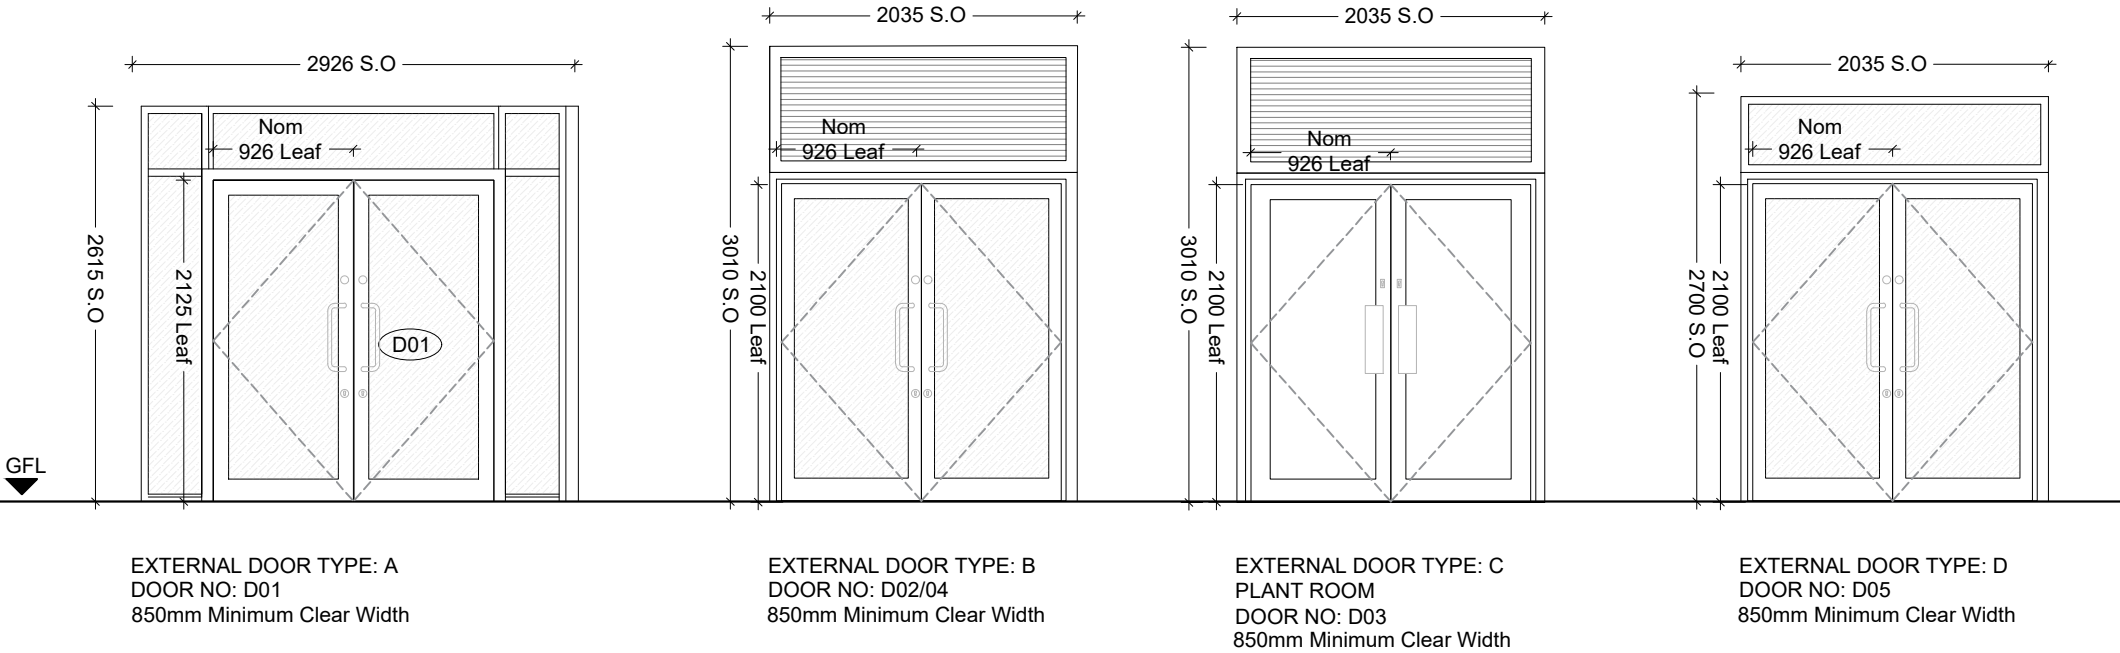

NOTES

1. filename: 1118 Door schedule.dwg

2. This drawing is not to be scaled. Use figured dimensions only. Detailed site survey to be carried out to establish tolerances. Figured dimensions are in mm. All dimensions shall be verified on site before proceeding with the work. The architect shall be notified of any discrepancies.

3. This drawing has been produced for sole use on this project and is not intended for use by any other person or for any other purpose. © Copyright RSS (U.K.)

4.

REVISIONS		
REV	DATE	STATUS
T01	02.10.25	Issued for Tender

Changes since last issue:

-

Notes:

- This drawing is issued for Tender purposes
- To be read alongside External Door Schedule

rivingtonstreetstudio

28 NAVIGATION ROAD LONDON E3 3TG

T : 020 7739 8945
E : rss@rssa.co.uk www.rivingtonstreetstudio.co.uk

job title	Stoke Park School Expansion					
drawing title	External Door Types					
scale	1:50@A3					
drawn by	job no.	suitability	revision			
CW	1118	D2	T01			
PROJECT	ORIGIN	VOLUME	LEVEL	TYPE	ROLE	NUMBER
SPS	RSS	_ 00	_ ZZ	_ DR	_ A	_ 4201