

GENERAL NOTES LEGEND:

GENERAL NOTES

READ IN CONJUNCTION WITH RELEVANT DRAWINGS. SPECIFICATIONS AND CURRENT BUILDING REGULATIONS APPROVED DOCUMENTS. ALL DIMENSIONS TO BE CONFIRMED ON SITE PRIOR TO CONSTRUCTION. DO NOT SCALE DRAWINGS TO OBTAIN DIMENSIONS. ALL DIMENSIONS TAKEN TO STRUCTURAL FACE OF MATERIAL OR GRID LINE AND DO NOT INCLUDE LININGS / FINISHES UNO. ADVISE OF ALL OMISSIONS / DISCREPANCIES AND AWAIT FURTHER INSTRUCTIONS. WALL BUILD UPS ARE INDICATIVE AND TO BE BUILT TO SUBCONTRACTOR DETAILS AND DESIGN. SEE 600 SERIES DETAILS FOR DESIGN INTENT.

READ IN CONJUNCTION WITH CONSULTANTS DRAWINGS FOR SETOUT AND COORDINATION OF:-
- STRUCTURAL WALLS, COLUMNS, STAIRS + SLAB
- SERVICE OPENINGS
- EXTERNAL DRAINAGE + ROADWORKS
- LANDSCAPING
- MECHANICAL & ELECTRICAL SERVICES

ALL SERVICES, DUCTING, RAINWATER PIPES AND DRAINAGE PIPES ARE SHOWN INDICATIVELY. CAPACITIES, SIZINGS AND SERVICE RUNS TO BE FULLY DESIGNED BY M+E CONSULTANT/CONTRACTOR.

PROPOSED LEVELS ARE PRELIMINARY ONLY AND TO BE DEVELOPED FURTHER BY THE CONTRACTOR AS PART OF THEIR CONSTRUCTION WORKS. CONTRACTOR TO SURVEY EXISTING DRAINAGE AND CONFIRM EXTENT OF WORKS REQUIRED TO SUIT PROPOSED LEVELS.

REFER TO ENGINEERS DRAWINGS FOR SIZE AND LOCATIONS OF ALL STRUCTURAL ELEMENTS.

PROPOSED LEVELS ARE PRELIMINARY ONLY AND TO BE DEVELOPED FURTHER BY THE CONTRACTOR AS PART OF THEIR CONSTRUCTION WORKS. CONTRACTOR TO SURVEY EXISTING DRAINAGE AND CONFIRM EXTENT OF WORKS REQUIRED TO SUIT PROPOSED LEVELS.

M+E NOTES

ALL SERVICES, DUCTING, RAINWATER PIPES AND DRAINAGE PIPES ARE SHOWN INDICATIVELY. CAPACITIES, SIZINGS AND SERVICE RUNS TO BE FULLY DESIGNED BY M+E CONSULTANT/CONTRACTOR.
RADIATOR LOCATIONS AND SIZES SHOWN INDICATIVELY.
REFER TO ENGDESIGN DRAWINGS FOR DETAILED HEATING LAYOUTS.
GAS METER BOX LOCATIONS INDICATIVE TO M&E DESIGN, DO NOT OBSTRUCT AIRBRICKS.

SETTING OUT NOTES

BUILDING SETOUT GRID POSITIONED BY S.ENG. ANY SETTING OUT INFORMATION SHOWN ON THIS DRAWING IS TO BE CROSS REFERENCED AND CHECKED AGAINST THE MEASURED SURVEY. ARKON ASSOCIATES ACCEPT NO RESPONSIBILITY FOR THE ACCURACY OF SURVEY WORK UNDERTAKEN BY OTHERS.

THIS DRAWING RELATES TO THE BUILDING SETOUT AND MAIN STATION POINTS AS PROVIDED ON SURVEYORS DRAWING. SURVEYORS REVI MODEL HAS BEEN USED AS A BASE MODEL FOR THIS DRAWING.

STRUCTURE & DRAINAGE
REFER TO STRUCTURAL ENGINEERS DRAWINGS FOR BLOCKWORK FIXING DETAILS TO RC COLUMNS AND WALLS, STRUCTURAL SLAB HEIGHTS AND UNDERGROUND DRAINAGE.

ELECTRICAL
ALWAYS SPACE 50mm BETWEEN OUTLET PLATES FOR EASE OF DECORATION. REFER TO BSEC ELECTRICAL LAYOUTS FOR DETAILED DESIGN.

WALL TYPE LEGEND

- EXT - Existing wall types as surveyed
- WT-A0 - Brickwork / Cavity Insulation / Block
- WT-A1 - Brickwork / Insulation / Stud
- WT-A2 - Zinc standing seam / Insulation / Stud
- WT-A3 - Brick slips / Blockwork
- WT-A4 - Render board / Blockwork / Render board
- WT-A5 - Brick slips / Cement board / Stud / Cement board / Brick slips
- WT-B - Plaster and acoustic board / Stud layer / Insulation / Stud / Plaster and acoustic board
- WT-B1 - Blockwork
- WT-B2 - Blockwork
- WT-B3 - Plaster and acoustic board / Stud layer
- WT-B4 - Block and acoustic board
- WT-C - Acoustic board / Stud / Acoustic board, ply noggins fixed to battens between studs to areas denoted on plans to receive fixtures
- WT-C1 - Acoustic board / Stud / Moisture board, ply noggins fixed to battens between studs to areas denoted on plans to receive fixtures
- WT-C2 - Acoustic boards / Stud
- WT-C3 - Fire resistant boards / Stud / Fire resistant boards
- WT-C4 - Acoustic board / Stud / Acoustic boards, noggins fixed to battens between studs to areas denoted on plans to receive fixtures
- WT-X - Brick slips / Brickwork (to be confirmed) / substructure to be confirmed. Overall width to match connecting wall
- WT-X0 - Brickwork (to be confirmed) / substructure to be confirmed. Overall width to match connecting wall
- WT-X1 - Brick slips / Brickwork (to be confirmed) / substructure to be confirmed. Overall width to match connecting wall


Windows Tags

- WE_00 Windows in existing openings replaced as new
- WN_00 Windows in new openings
- WL_00 Louvers to smoke shaft

© ARKON ASSOCIATES LTD.

THIS DRAWING IS THE PROPERTY OF ARKON ASSOCIATES LTD. AND IS ISSUED ON THE CONDITION THAT IT IS NOT REPRODUCED, DISCLOSED OR COPIED TO ANY UNAUTHORISED PERSON IN WHOLE OR IN PART WITHOUT PRIOR WRITTEN CONSENT. NO DIMENSIONS ARE TO BE SCALED FROM THIS DRAWING. ALL DIMENSIONS STATED MUST BE VERIFIED ON SITE. THE ARCHITECT MUST BE ADVISED OF ANY DISCREPANCIES PRIOR TO ANY ITEM OF WORK BEING PUT IN HAND OR EXECUTED. THIS DRAWING MUST BE READ TOGETHER WITH THE SPECIFICATION, BILL OF QUANTITIES AND RELATED DRAWINGS

Rev	Date	By	Checked	Description
01	17.02.2026	GM	LJC	Scheme updated to coordinate with Structural Design

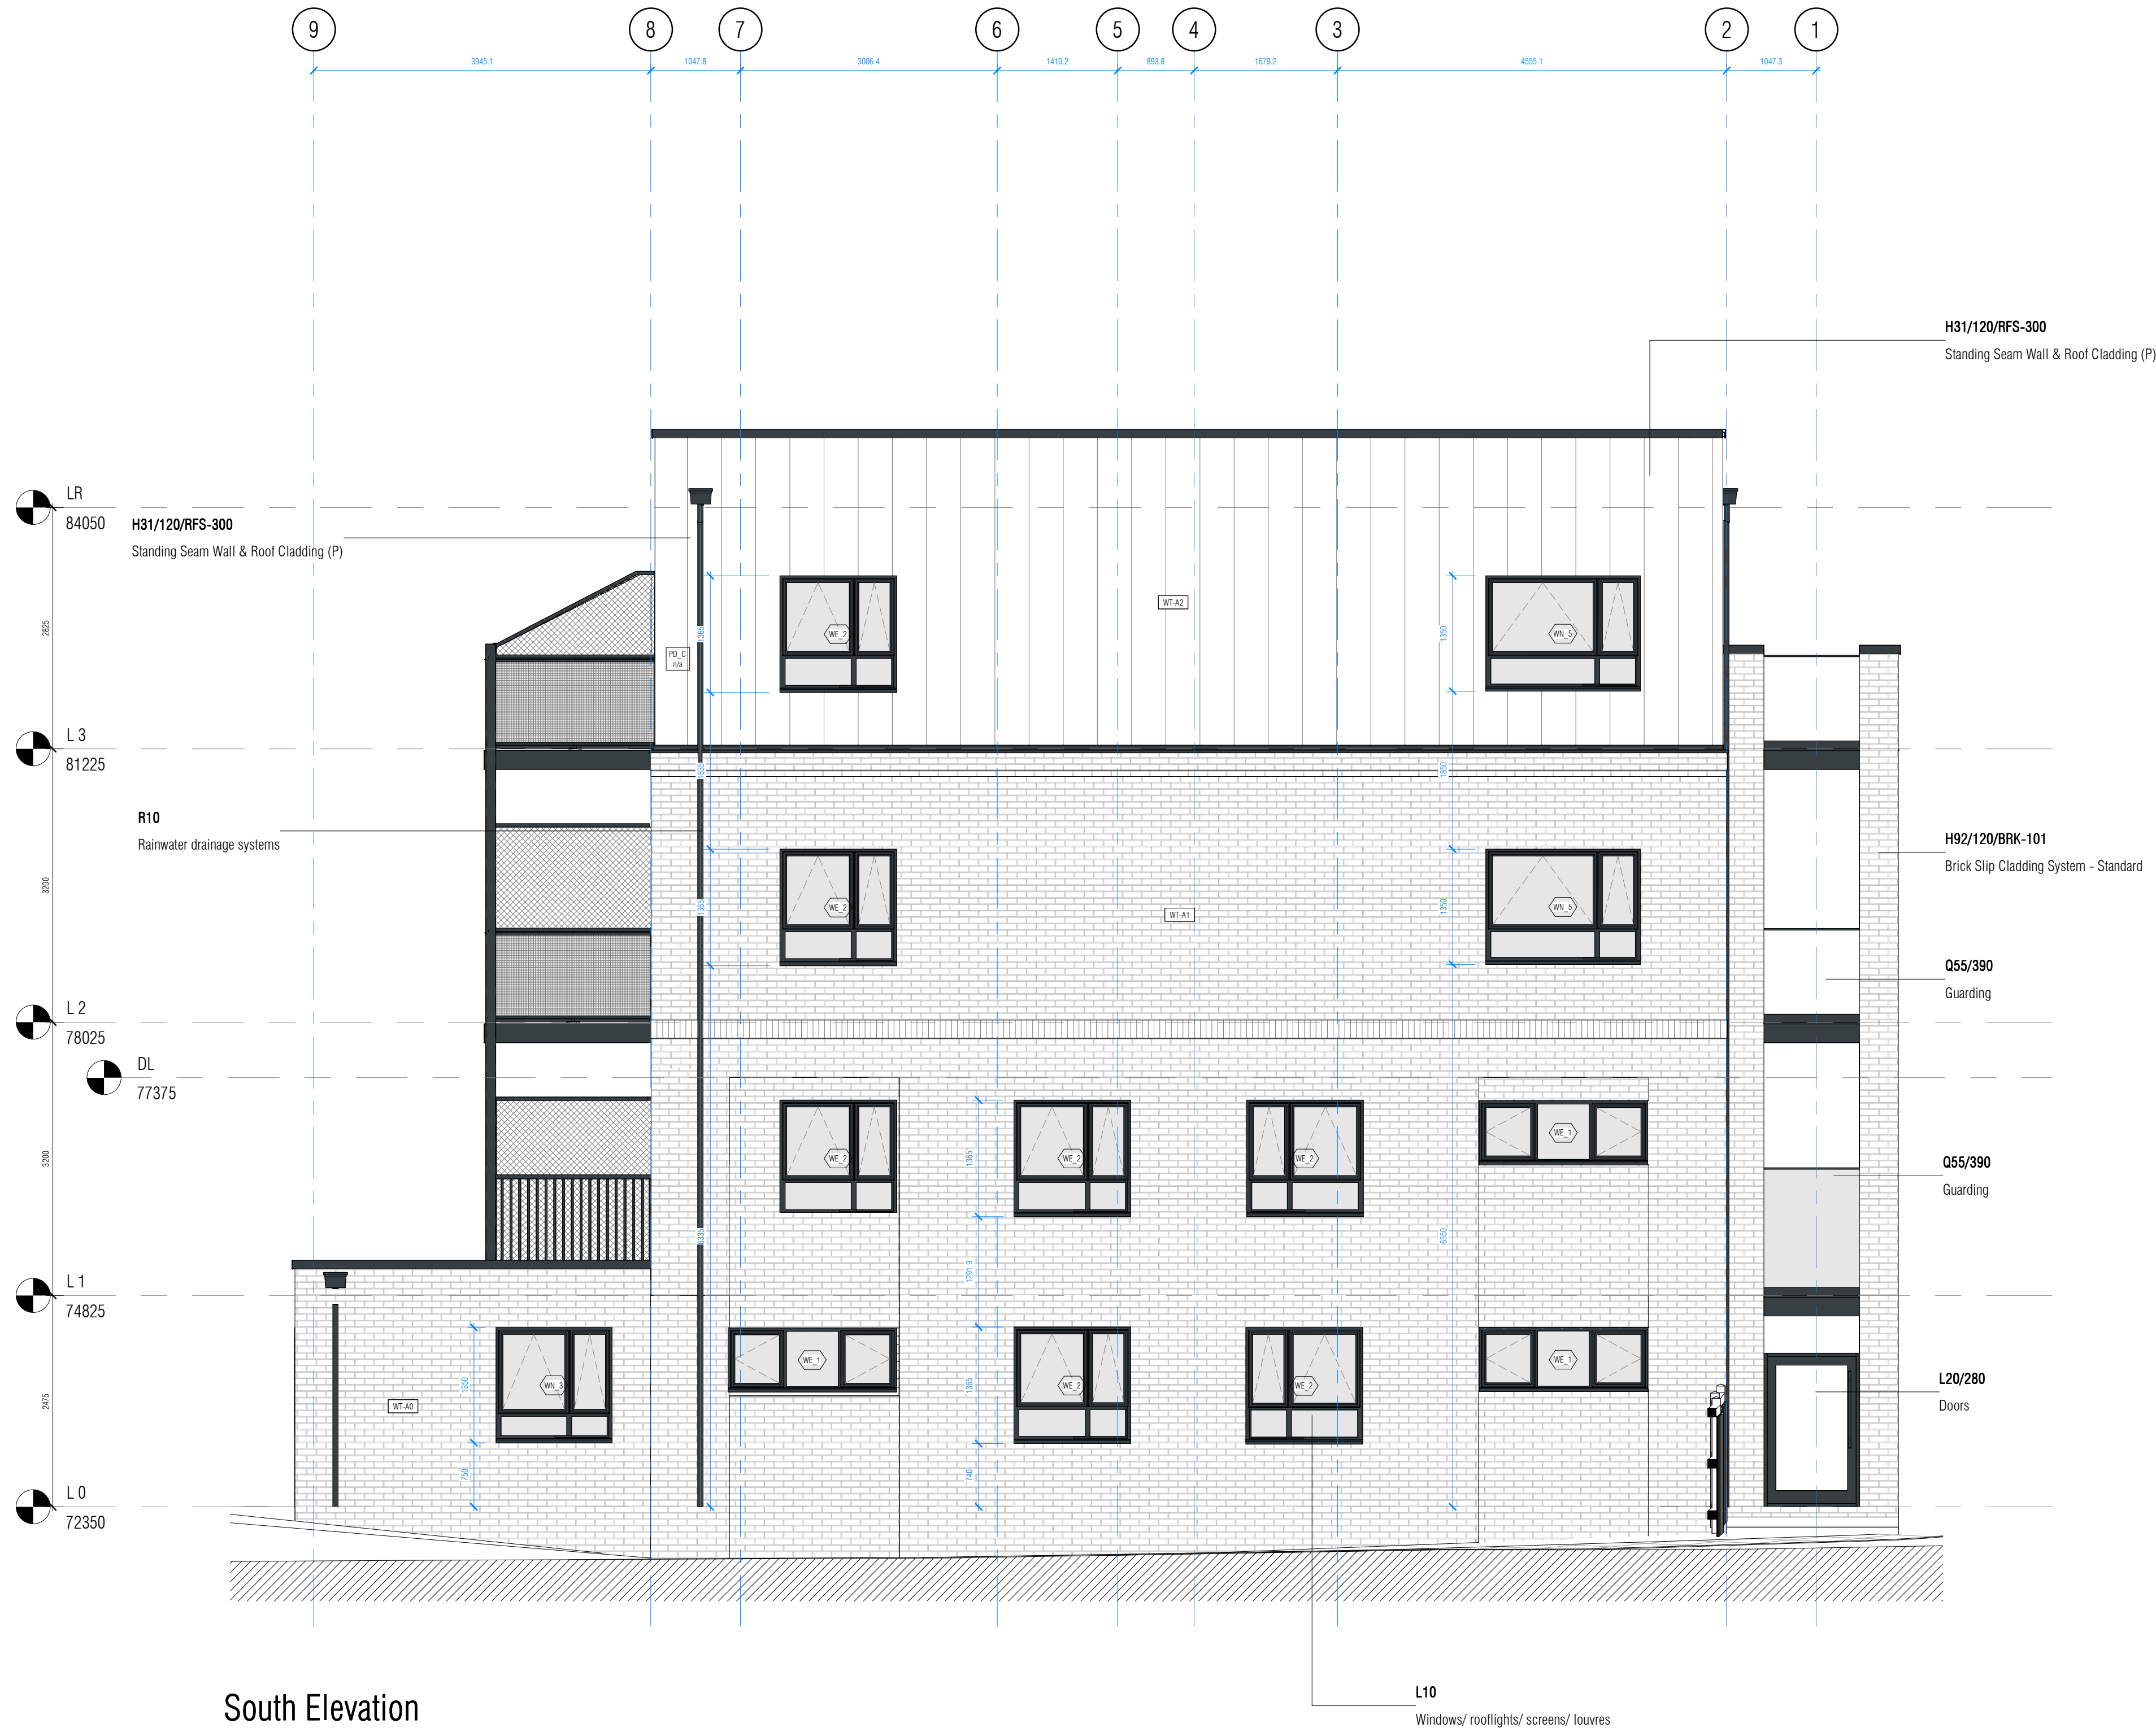

South Elevation

1 : 50

Scale 1:50 0 1 2.5 5m

CLIENT:		TITLE:		
		South Elevation Setting Out		
PROJECT:	SCALE	DATE	DRAWN BY:	CHECKED:
Gordon Court, Stonegrove Edgware, HA8 7TQ	As indicated @A1	15.12.2022	GM	AB
ISSUE STATUS:	PROJECT No:	DWG No:	REV:	
TENDER	5244	A21107	01	



ARKON ASSOCIATES LIMITED
Luminous House,
300 South Row,
Milton Keynes, Bucks.
MK9 2FR.

T: +44(1438)359816
E: enquiries@arkonassociates.co.uk
W: www.arkonassociates.co.uk

arkonassociates
architecture + design