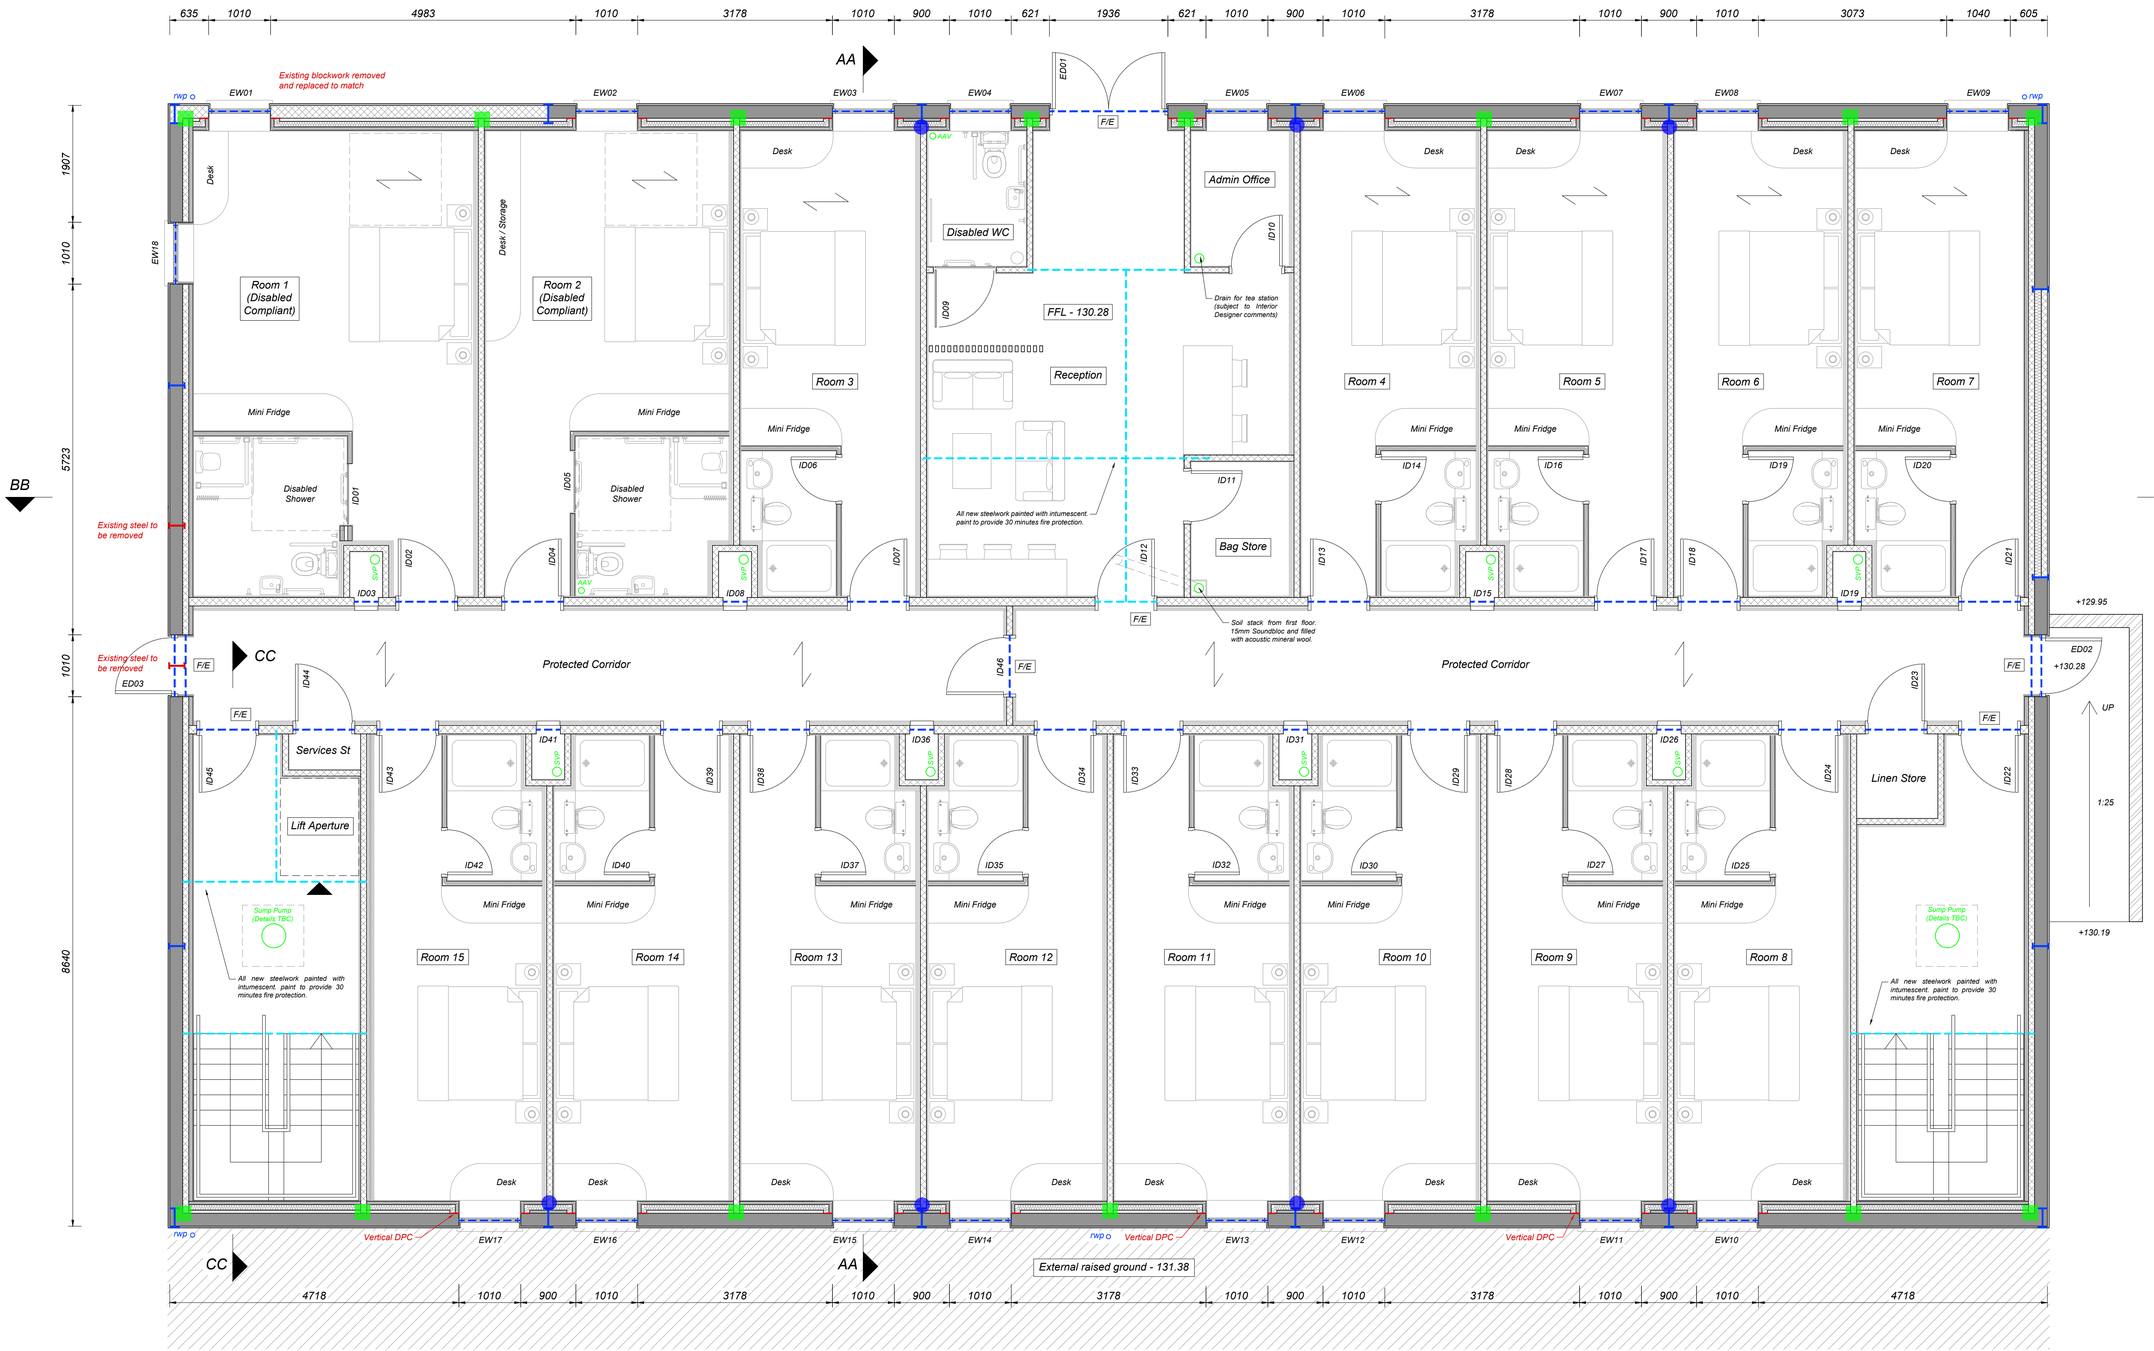

Do not scale from this drawing, work to given dimensions. All dimensions to be checked on site. Any discrepancies with this drawing to be reported and clarified prior to commencing work on site. ADM Surveyors Ltd accept no responsibility for works not undertaken fully in accordance with this drawing and relevant specifications.

Copyright © ADM Surveyors Limited

North Point:

Notes:

Part M Notes:

The reception desk or counter should have a clear manoeuvring space in front of the desk or counter of 1200mm deep and 1800mm wide if there is a knee recess of 500mm deep or 1400mm deep and 2200mm wide if there is no knee recess. The reception desk or counter should be designed to accommodate both standing and seated visitors such that at least one section of the counter has a drop down area at least 1500mm wide with its surface no higher than 760mm and a knee recess not less than 700mm above finished floor level. There should be a hearing enhancement system such as an induction loop.

Revision Log:

Rev:	Description:	By:	Date:

Project:
Berryfields Farm
Berkswell Road
Meriden
Coventry
CV7 7LB

Client:
Chris Barber Limited
Berryfields Farm
Berkswell Road
Meriden
Coventry
CV7 7LB

Scale: 1:50

Drawing Issue: Tender

Date: 19.03.2024

Drawn by: TR

Checked by: SK

Paper Size: A1

Drawing Title: Proposed Ground Floor Plan

Drawing Number: 3847.T05

Revision Number: /

ADM Surveyors

Chartered Quantity & Building Surveyors

Suite 1, Rosehill, 165 Lutterworth Road,
Blaby, Leicester, LE8 4DX
Tel: 0116 2775827

www.admsurveyors.co.uk

RICS LABC CIAT CHARTERED PRACTICE