


South Eastern Elevation

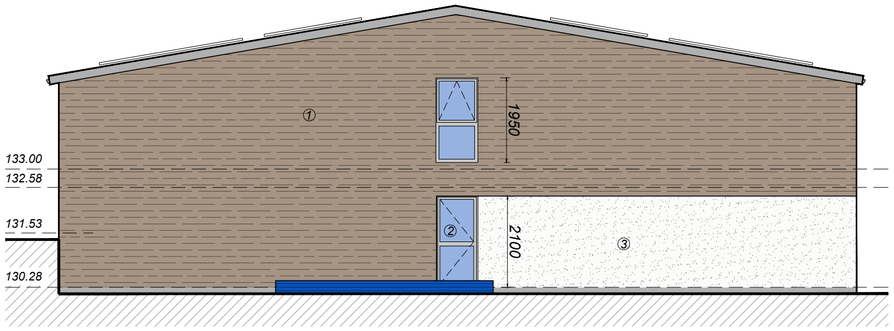


North Western Elevation




South Western Elevation

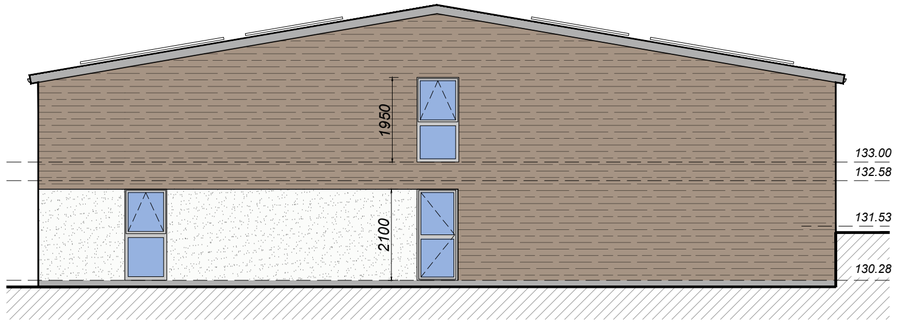


North Eastern Elevation

Do not scale from this drawing, work to given dimensions. All dimensions to be checked on site. Any discrepancies with this drawing to be reported and clarified prior to commencing work on site. ADM Surveyors Ltd accept no responsibility for works not undertaken fully in accordance with this drawing and relevant specifications.

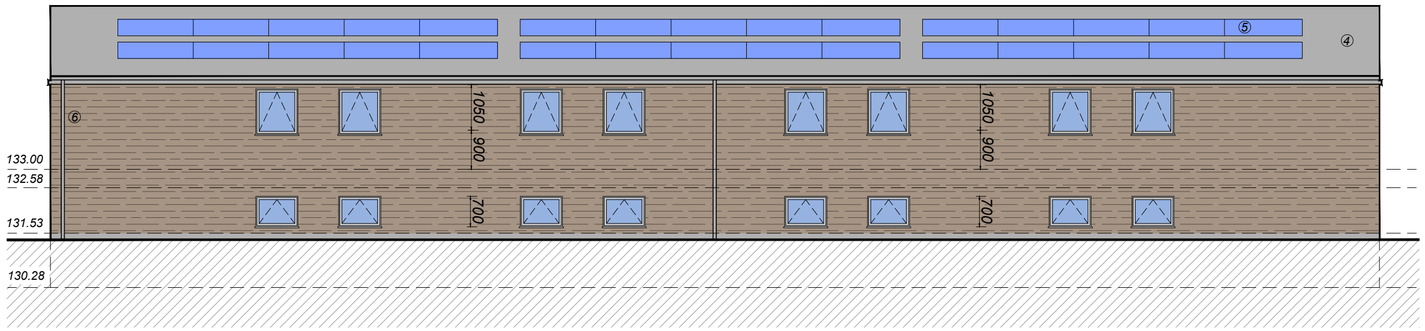Copyright © ADM Surveyors Limited

**North Point:**

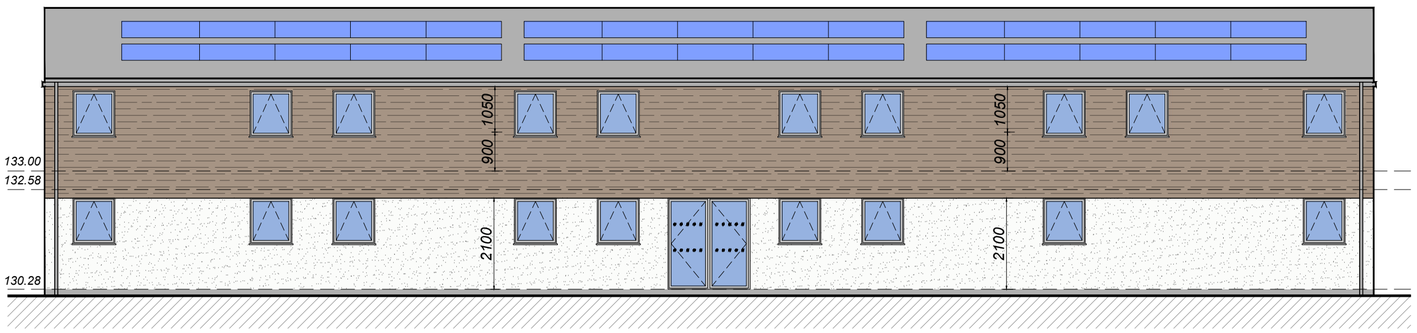**Notes:**

External Finishes:

1. Waney edge cladding board to match the existing restaurant building. To be installed on vertical timber battens fixed to the existing masonry wall.
2. Double glazed aluminium windows and doors. Colour RAL 7016.
3. 25 x 50mm timber battens with render carrier board. Insect mesh required at low level. Through colour render finish.
4. New Kingspan Topdek roof panel (138mm overall) finished with Sikaplan SGK PVC membrane.
5. Solar panels by specialist.
6. New Alumasc GX Pressed Aluminium box gutters 140 x 100mm with 100mm downpipes.

**Revision Log:**

| Rev: | Description: | By: | Date: |
|---|---|---|---|
| | | | |

**Project:**
Berryfields Farm
Berkswell Road
Meriden
Coventry
CV7 7LB

**Client:**
Chris Barber Limited
Berryfields Farm
Berkswell Road
Meriden
Coventry
CV7 7LB

**Scale:** 1:100

**Drawing Issue:** Tender

**Date:** 19.01.2024

**Drawn by:** TR

**Checked by:** SK

**Paper Size:** A2

**Drawing Title:** Proposed Elevations

**Drawing Number:** 3847.T07

**Revision Number:** /

ADM Surveyors

**Chartered Quantity & Building Surveyors**

Suite 1, Rosehill, 165 Lutterworth Road, Blaby, Leicester, LE8 4DX
Tel: 0116 2775527
www.admsurveyors.co.uk

RICS LABC CIAT CHARTERED PRACTICE